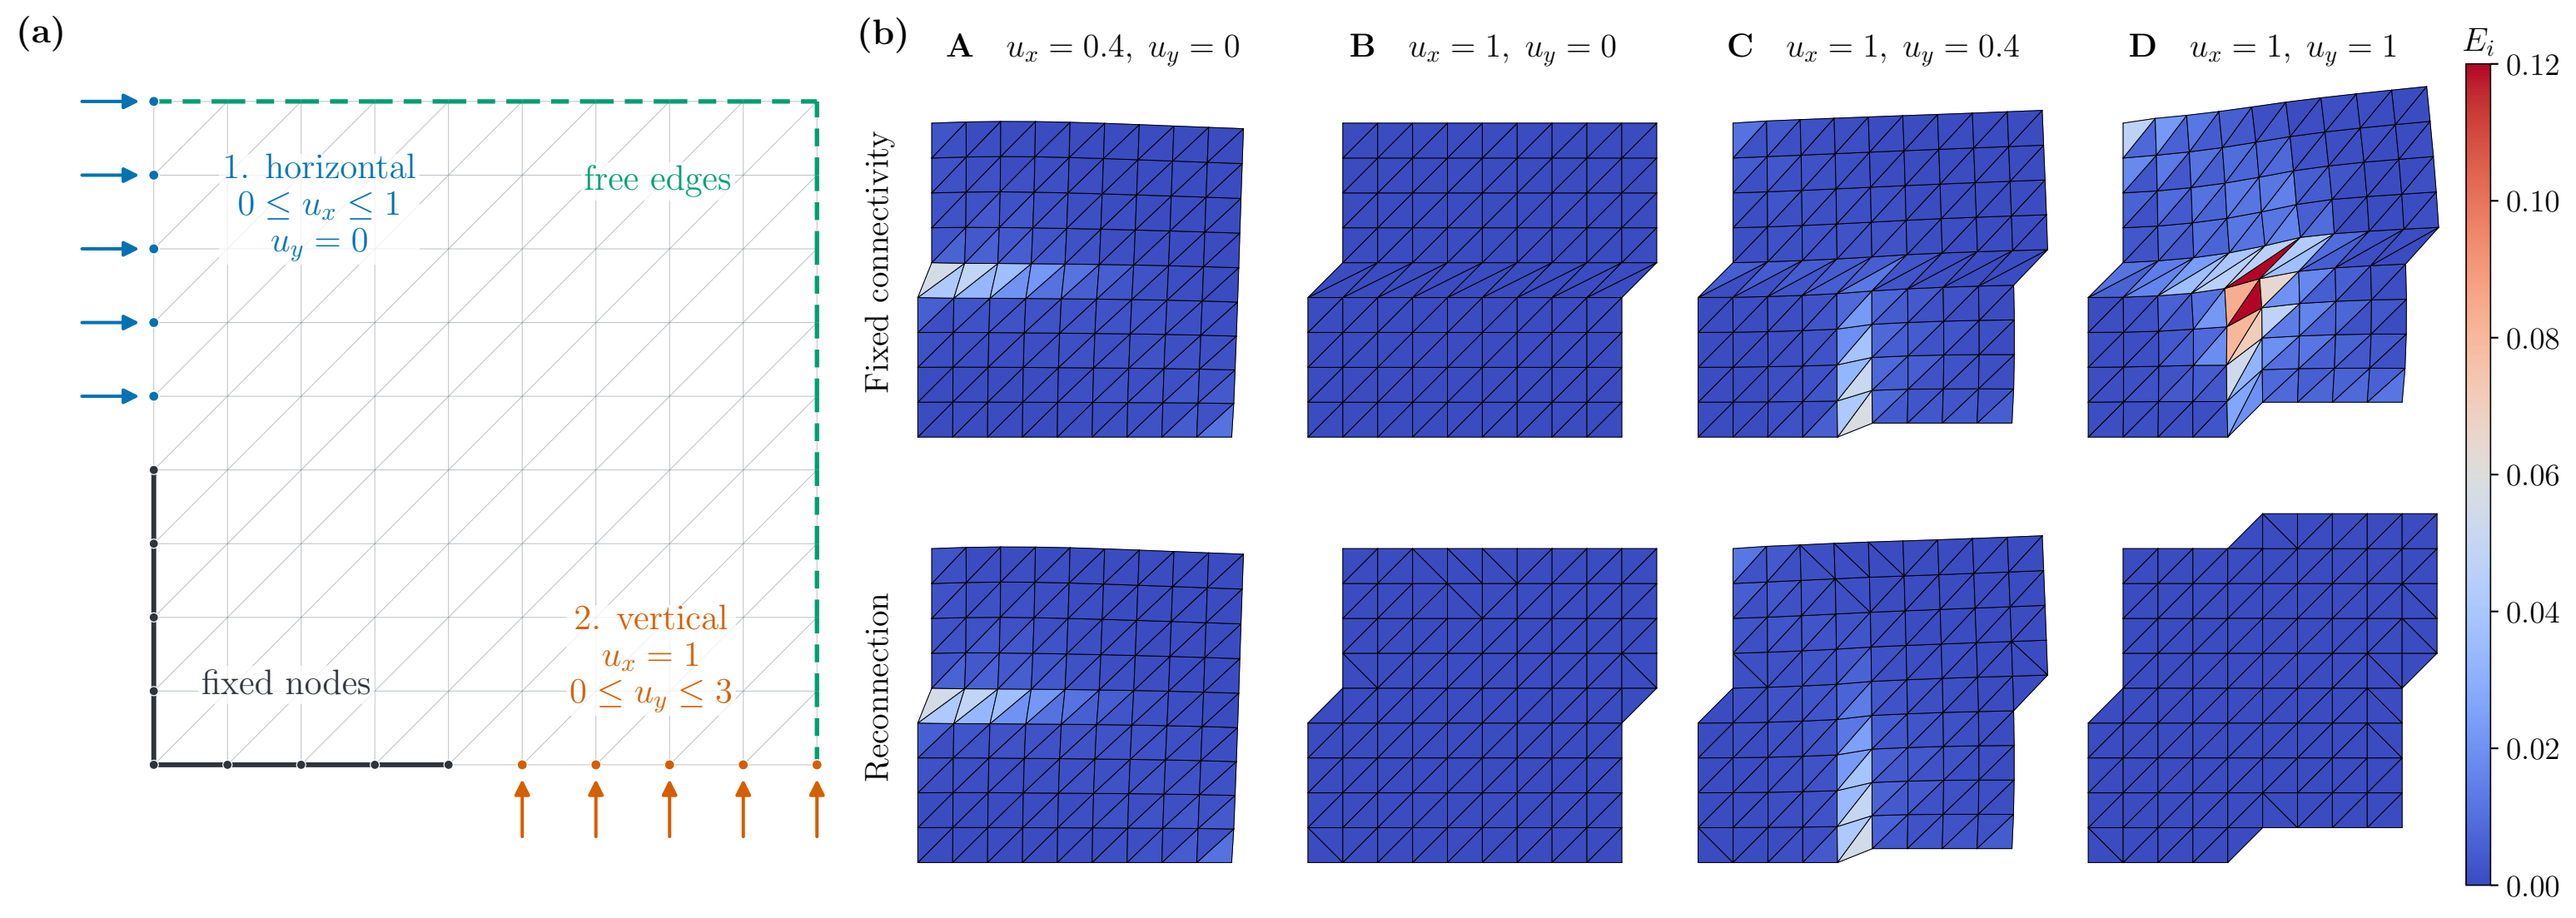

(a)
1. horizontal
$0 \leq u_x \leq 1$
$u_y = 0$
free edges
fixed nodes
2. vertical
$u_x = 1$
$0 \leq u_y \leq 3$
(b)
A $u_x = 0.4,\ u_y = 0$
B $u_x = 1,\ u_y = 0$
C $u_x = 1,\ u_y = 0.4$
D $u_x = 1,\ u_y = 1$
Fixed connectivity
Reconnection
E_i
0.12
0.10
0.08
0.06
0.04
0.02
0.00